
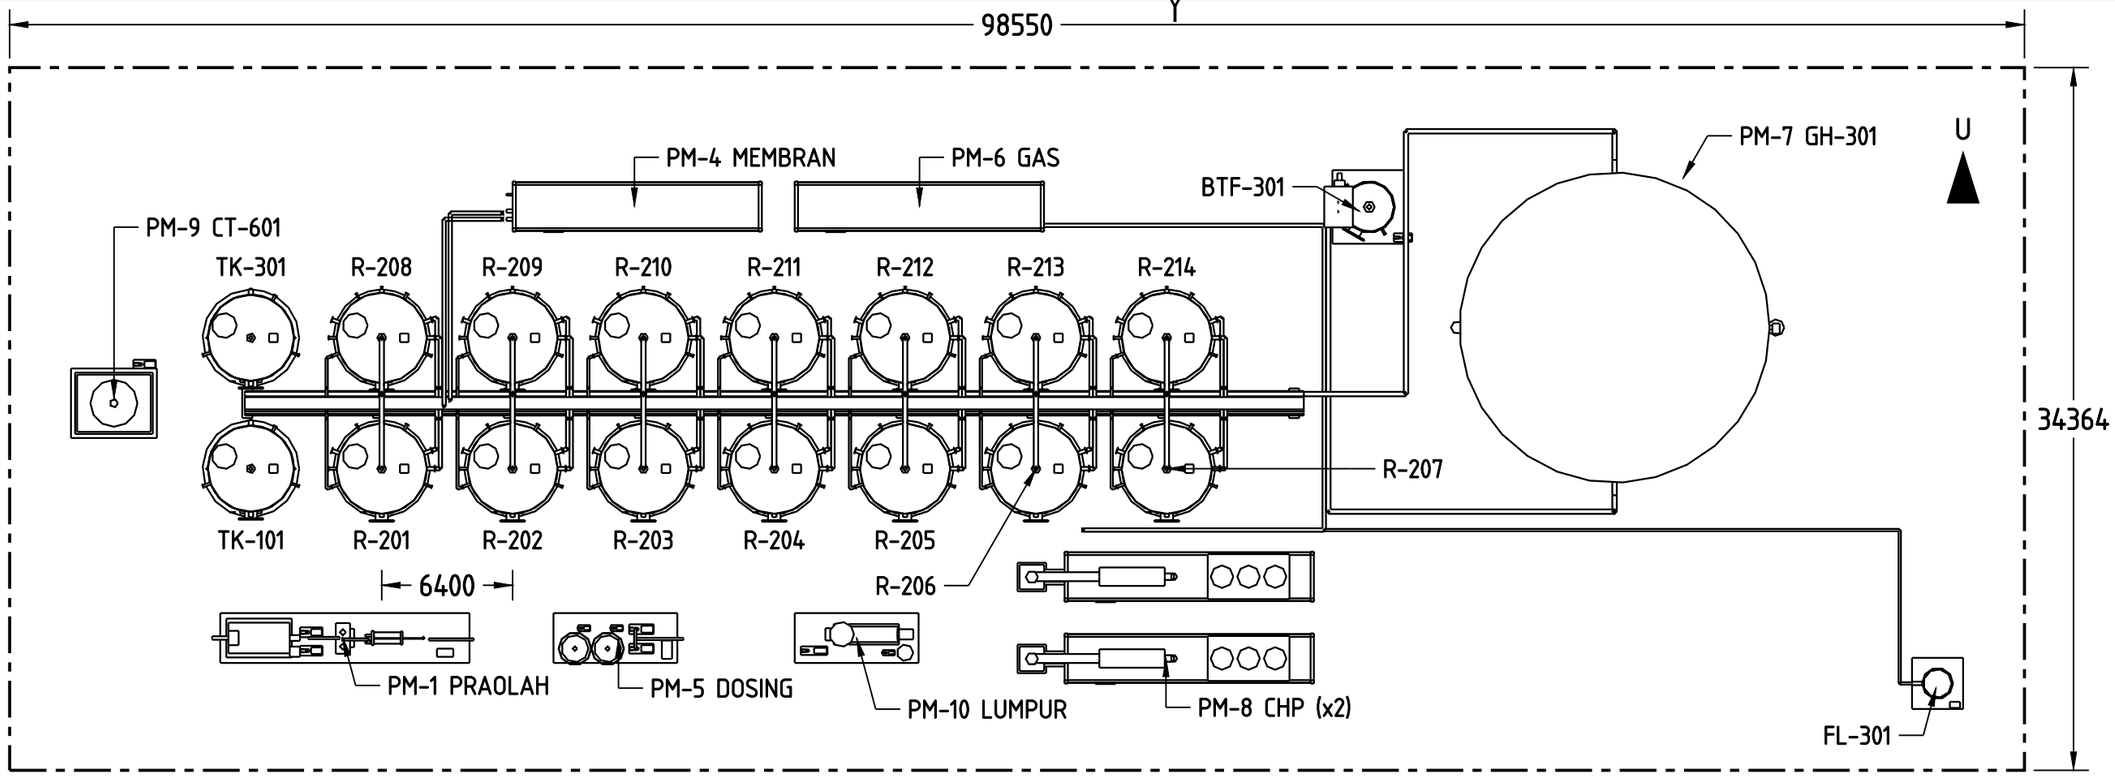


DENAH TATA LETAK (DARI MODEL 3D)

SKALA 1:300

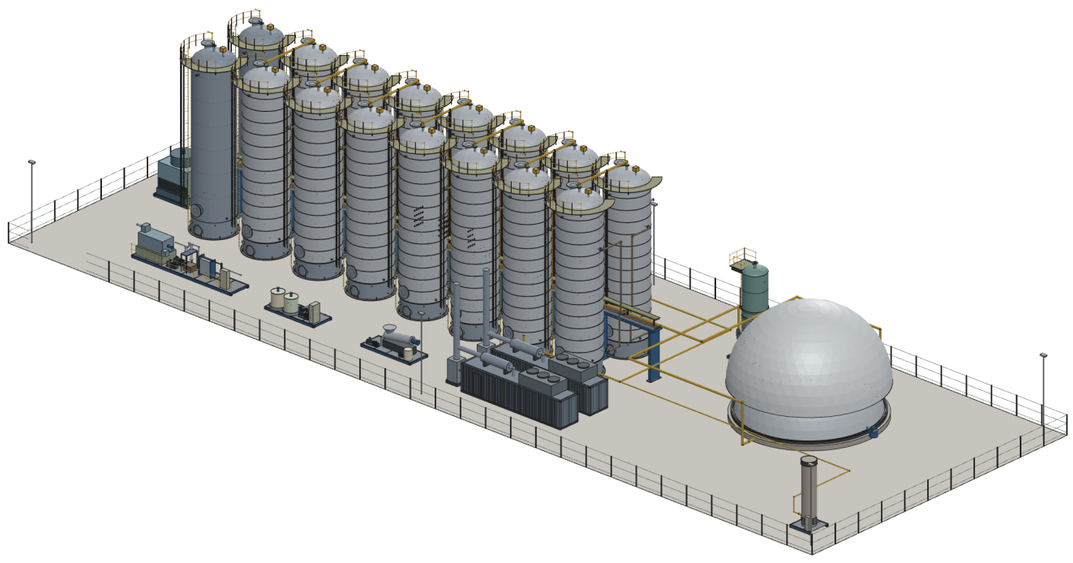

ISOMETRI SUSUNAN PABRIK (TANPA SKALA)

SET MODUL PORTABEL				
Modul	Nama	Jml	Pengiriman	Massa t
PM-1	Skid praolah POME	1	kontainer 40 ft (skid)	12.0
PM-2	Tangki penyangga umpan	1	bejana di trailer low-bed	19.0
PM-3	Reaktor AnMBR termofilik	14	bejana di trailer low-bed	266.0
PM-4	Kontainer membran + CIP	1	kontainer 40 ft HC	16.0
PM-5	Skid dosing dan pompa umpan	1	skid 20 ft	8.0
PM-6	Skid pengolahan biogas	1	kontainer 40 ft + bejana BTF	14.0
PM-7	Penampung gas + flare	1	kontainer 20 ft + skid flare	7.0
PM-8	Kontainer CHP	2	kontainer 40 ft HC	48.0
PM-9	Skid pemulih panas + menara pendingin	1	skid 20 ft + sel CT modular	9.0
PM-10	Tangki permeat + skid lumpur	1	bejana + skid 20 ft	27.0

Total 28 muatan truk, ± 426 t. Plot 98.5 x 34.4 m = 0.34 ha (termasuk jalan 3 m).

SKALA SET (DESAIN BEJANA SAMA)					
PKS	Reaktor	Genset	Neto kWe	GWh/thn	Membran m²
30 t/jam	10	2 x 600 kWe	627	4.5	634
45 t/jam	14	2 x 800 kWe	961	6.9	996
60 t/jam	19	3 x 600 kWe	1311	9.4	1314

University: UNIVERSITAS	Checked by : -	Design Lab.	Document type: General Arrangement			Rev: 0
	Author : NAMA TIM	Tata Letak Umum Set Portabel PKS 45 t TBS/jam	Unit: mm	Scale: 1 : 300	Creation date: 15/10/2026	Size: A3
	Eng. Approved by : -		BG-GA-001			Sheet number: 1 / 9