

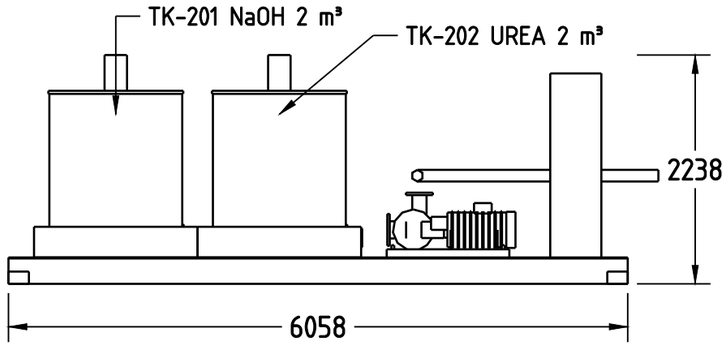



PM-5 TAMPAK DEPAN 1:60

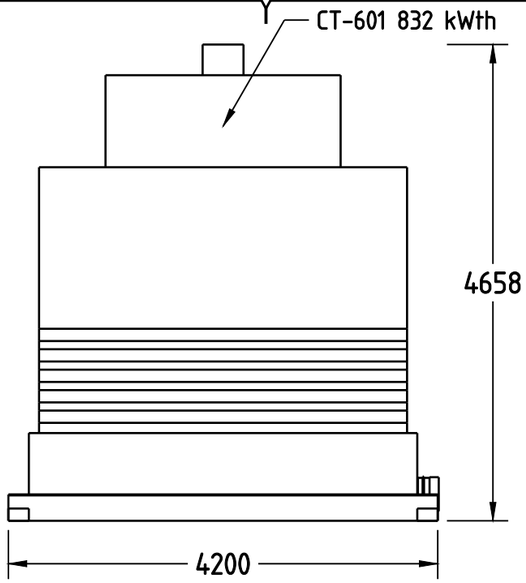


PM-9 TAMPAK DEPAN 1:60

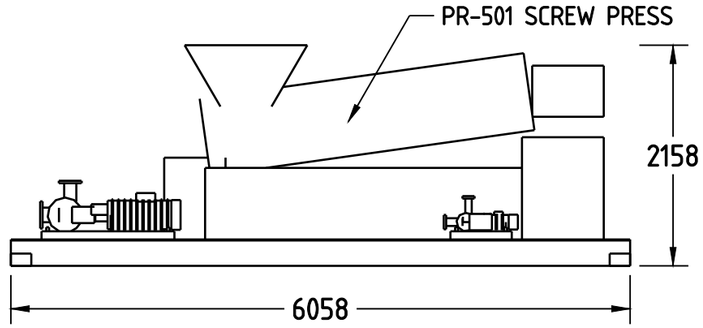


PM-10 TAMPAK DEPAN 1:60

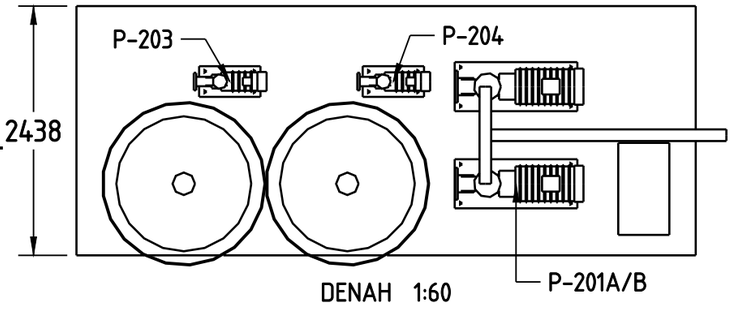


DENAH 1:60

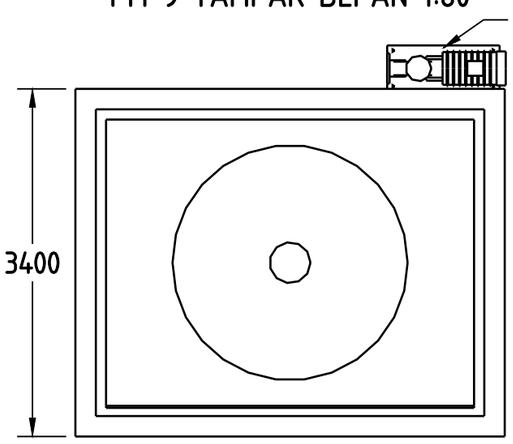


DENAH 1:60

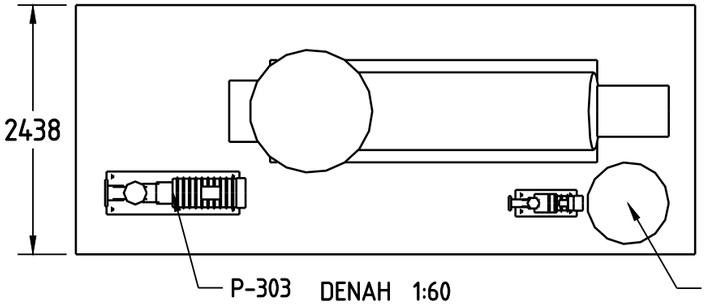


DENAH 1:60

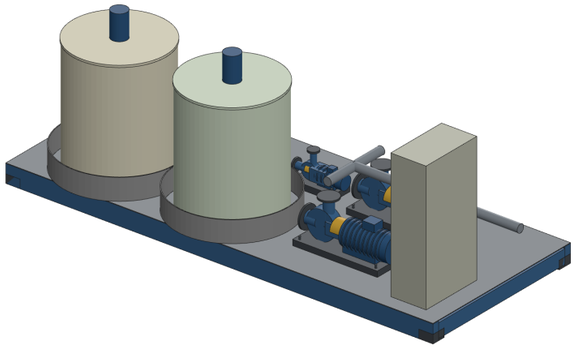

ISOMETRI PM-5

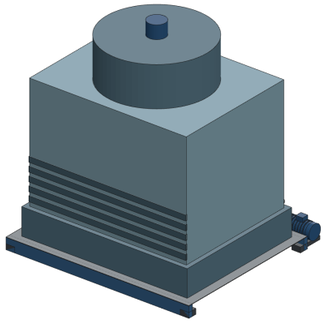

ISOMETRI PM-9

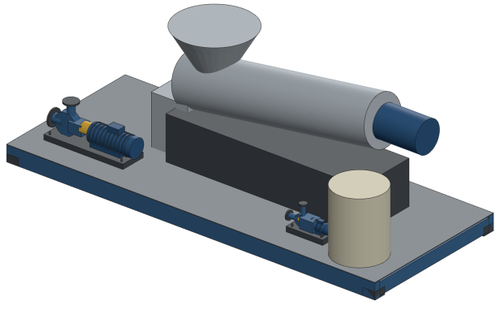

ISOMETRI PM-10

DAFTAR BAGIAN SKID				
Skid	Tag	Uraian	Bahan / daya	kg
PM-5	TK-201/202	Tangki NaOH / urea 2 m³	HDPE + bund	2x260
	P-201A/B	Pompa umpan reaktor	CF8M, 7,5 kW	2x260
	P-203/204	Pompa dosing	PVDF, 0,37 kW	2x45
	-	Panel dosing + skid 20 ft	IP65 / S275	2080
PM-9	CT-601	Menara pendingin 832 kWth	FRP, 7,5 kW	2900
	P-601	Pompa air pendingin	GG25, 11 kW	210
	-	Skid 4200 x 3400	S275 galv.	1500
PM-10	P-303	Pompa lumpur (progressive cavity)	CS/NBR, 4 kW	380
	PR-501	Screw press lumpur	SS304, 5,5 kW	2600
	TK/P-polimer	Tangki + pompa polimer 1 m³	HDPE / PVDF	160
	-	Skid 20 ft + chute kue	S275 galv.	1900

University: UNIVERSITAS	Checked by : -	Design Lab.	Document type: Assembly Drawing			Rev: 0
	Author : NAMA TIM	Skid PM-5, PM-9 dan PM-10 (Dosing, CT-601, Lumpur)	Unit: mm	Scale: 1 : 60	Creation date: 15/10/2026	Size: A3
	Eng. Approved by : -		BG-M-005			Sheet number: 8 / 9