

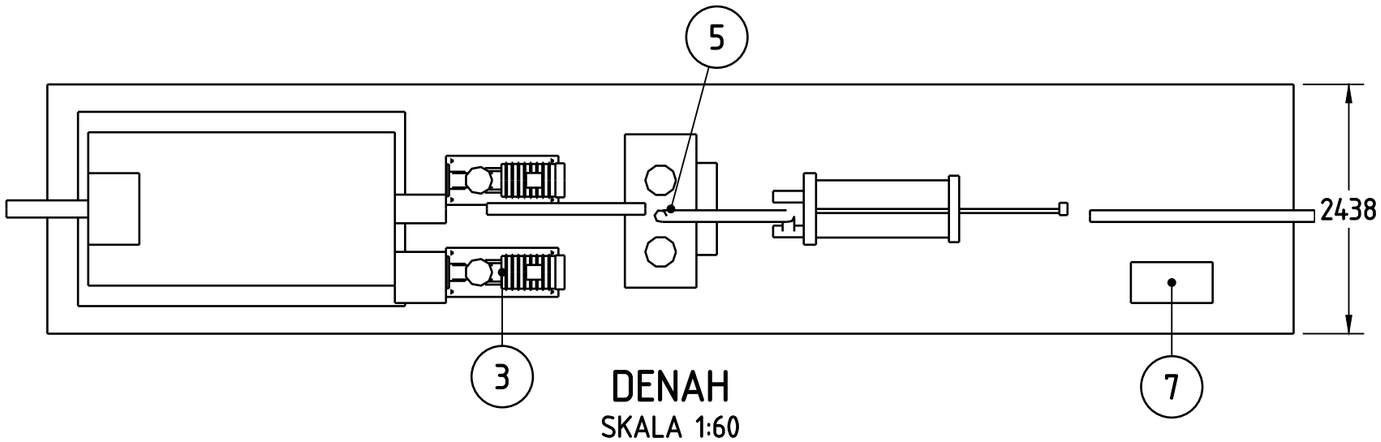



DENAH
SKALA 1:60

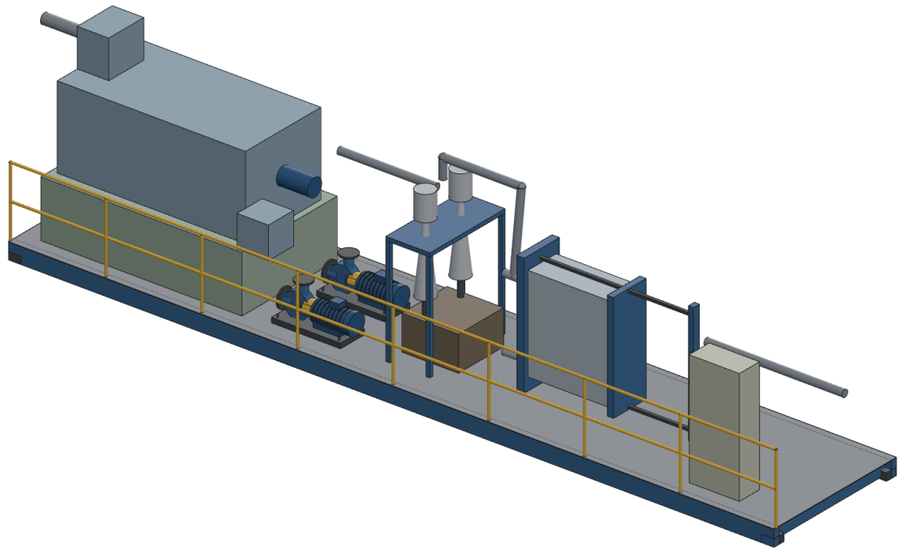

ISOMETRI (TANPA SKALA)

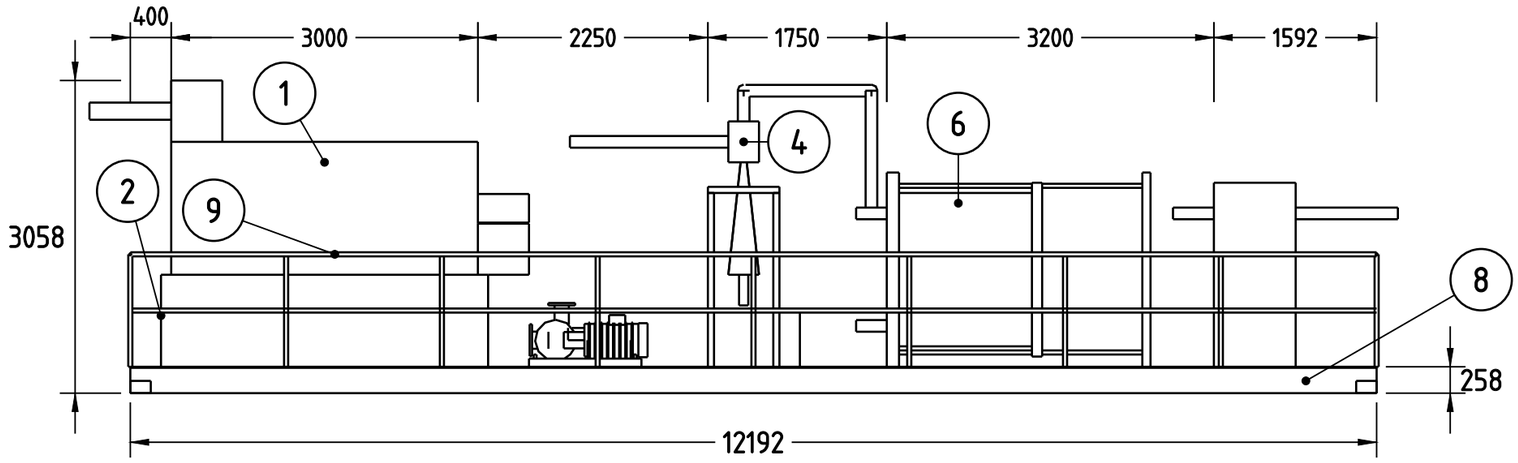

TAMPAK DEPAN
SKALA 1:60

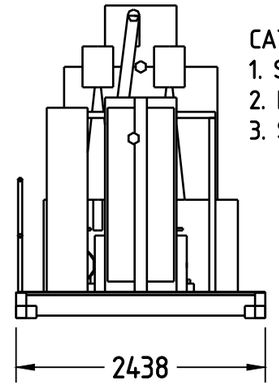

TAMPAK UJUNG
SKALA 1:60

CATATAN :
1. Seluruh alat dirakit & diuji di bengkel.
2. Pengiriman: 1 truk trailer 40 ft, ± 12 t.
3. Sambungan: POME masuk DN150 (kiri), POME keluar DN100 ke TK-101 (kanan).

DAFTAR BAGIAN

No	Tag	Uraian	Bahan	Jml	kg
1	SC-101	Saringan drum Ø900x2600, 0,75 mm	SS304	1	1450
2	–	Bak sump 3 m³	SS304 t4	1	620
3	P-101A/B	Pompa desander H 20 m, VSD	CD4MCu, 11 kW	2	2x310
4	HC-101	Hidrosiklon Ø300	PU-lined CS	2	2x140
5	–	Bak pasir 0,4 m³	S275 galv.	1	180
6	E-101	PHE 812 kWth	SS316/EPDM	1	1850
7	–	Panel kontrol lokal	IP65	1	220
8	–	Skid UNP 250 12192x2438	S275, cat	1	3900
9	–	Pegangan tangan Ø42,4	S275 galv.	1	240
10	–	Pipa, katup, kabel	SS304 / PVC	1 lot	1100

SAMBUNGAN SKID

Tag	Ukuran	Layanan	Dari → ke
N-A	DN150	POME panas masuk (85 °C)	PKS → SC-101
N-B	DN100	POME tersaring ke TK-101	E-101 → TK-101
N-C	DN80	Air pendingin masuk / keluar	CT-601 ↔ E-101
N-D	DN50	Underflow pasir	HC-101 → bak
N-E	–	Daya 400 V, 3 fasa, 45 kVA	MCC → panel

University: UNIVERSITAS	Checked by : –	Design Lab.	Document type: Assembly Drawing	Rev: 0
	Author : NAMA TIM	PM-1 Skid Praolah POME (SC-101, HC-101, E-101)	Unit: mm / Scale: 1 : 60 / Creation date: 15/10/2026	Size: A3
	Eng. Approved by : –		BG-M-001	Sheet number: 4 / 8