
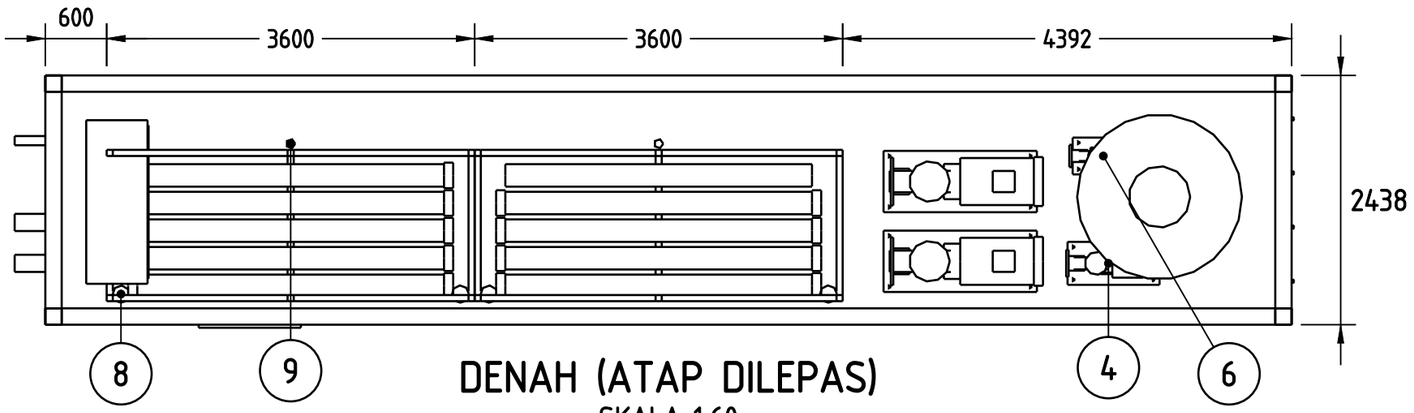



DENAH (ATAP DILEPAS)

SKALA 1:60

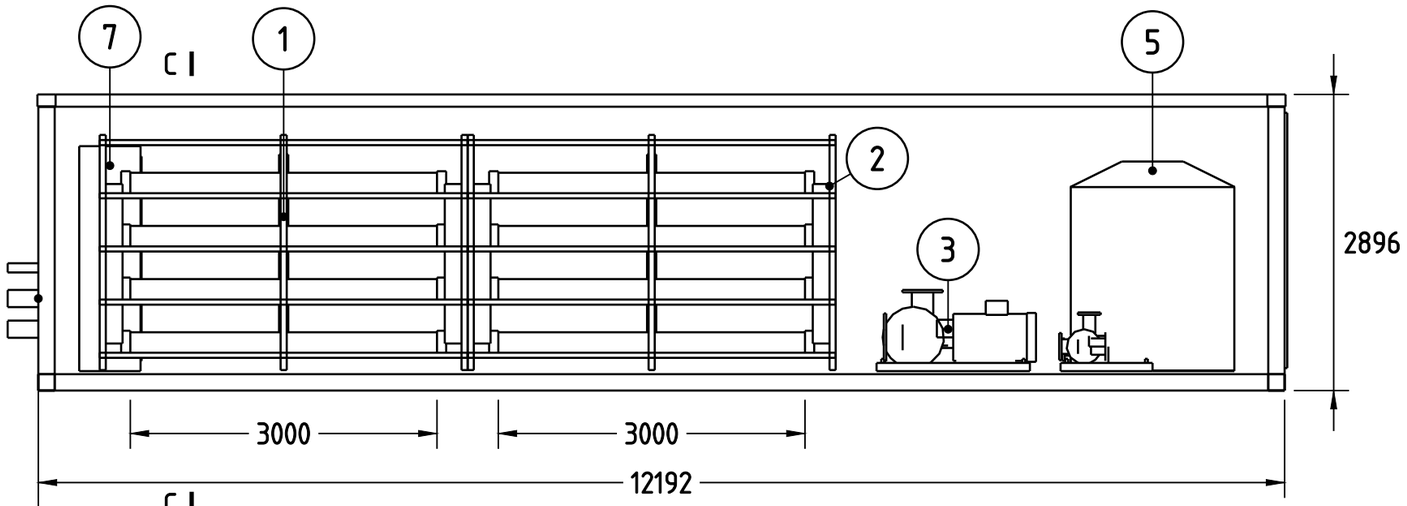

TAMPAK SAMPING (DINDING DILEPAS)


SKALA 1:60

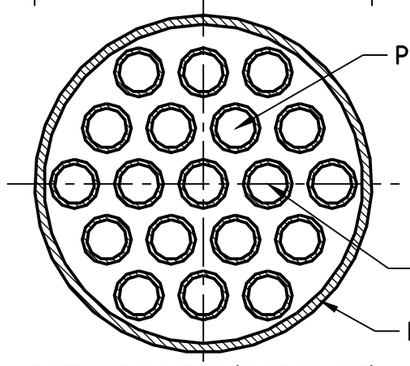

POTONGAN C-C (MODUL UF)
SKALA 1:4

CATATAN :

1. 2 bank x 5 kolom x 4 tingkat (40 posisi), 34 terpasang + 6 cadangan.
2. Fluks 15 LMH, luas 996 m², cross-flow 4 m/s.
3. Lorong servis 850 mm di sisi pompa.
4. Dinding kiri & atap dilepas untuk kejelasan.
5. CIP: NaOCl 500 ppm + asam sitrat 2 %, tiap 30 hari.

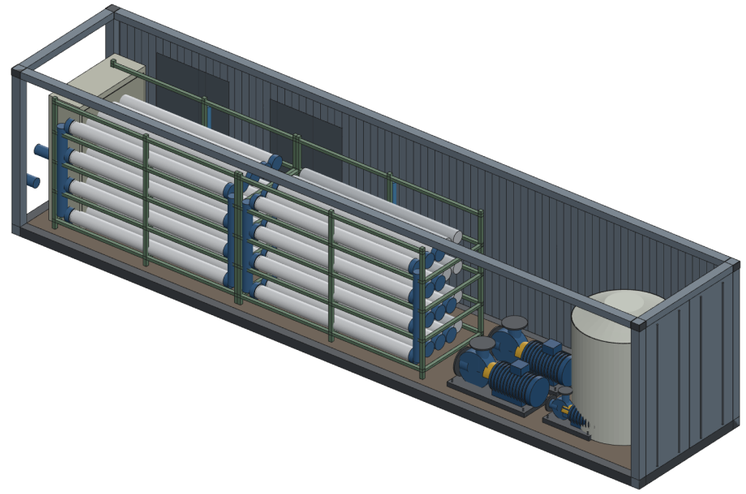


ISOMETRI POTONG (TANPA SKALA)

DAFTAR BAGIAN

No	Tag	Uraian	Bahan	Jml	kg
1	MB-301	Modul UF tubular Ø220x3000, 30 m²	PVDF/PVC-U	34	2108
2	–	Rak modul 2 bank	S275 galv.	2	1450
3	P-301A/B	Pompa cross-flow 149 m³/jam	CF8M, 30 kW	2	2x520
4	P-302	Pompa permeat	CF8M, 5,5 kW	1	140
5	TK-302	Tangki CIP 4 m³	SS304	1	380
6	P-304	Pompa CIP	CF8M, 4 kW	1	110
7	–	Panel MCC + PLC	IP54, VSD	1	650
8	–	Header umpan/retentat DN150	SS316L Sch10S	4	4x60
9	–	Header permeat DN80	PVC-U PN10	2	2x15
10	–	Nosel dinding DN150/80	SS316L	3	3x25
11	–	Kontainer ISO 40 ft HC	Corten, insul.	1	4200
12	–	Pipa, katup, kabel, CIP	–	1 lot	900

Total kering ± 12,1 t; transport ± 16 t (berisi air uji).

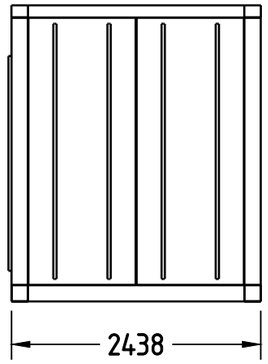

TAMPAK UJUNG

SKALA 1:60

University: UNIVERSITAS	Checked by : –	Design Lab.	Document type: Assembly Drawing		Rev: 0
	Author : NAMA TIM	PM-4 Kontainer Membran UF (MB-301, P-301, P-302, TK-302)	Unit: mm	Scale: 1 : 60	Creation date: 15/10/2026 / Size: A3
	Eng. Approved by : –		BG-M-004		Sheet number: 3 / 8