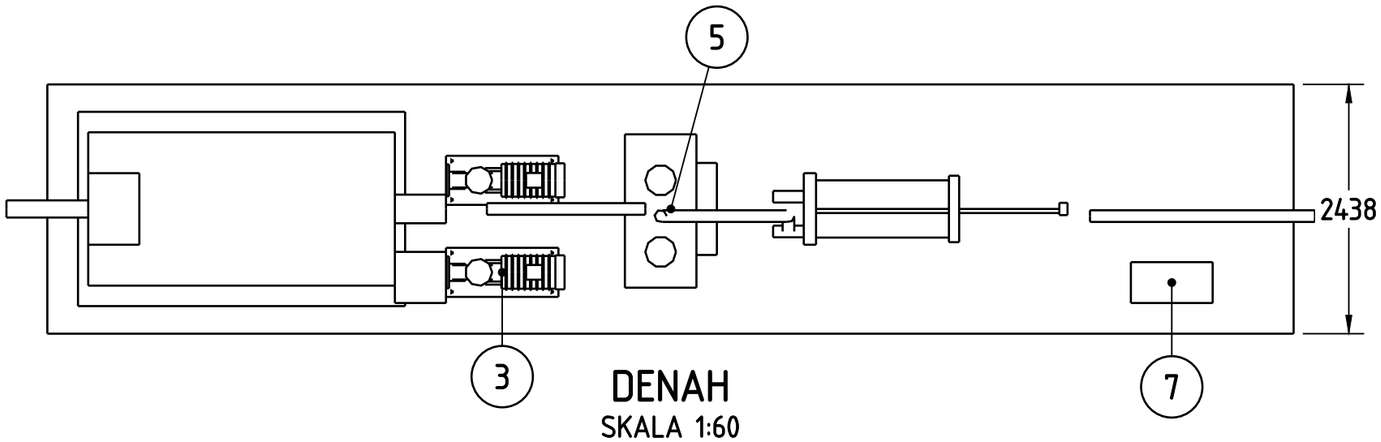
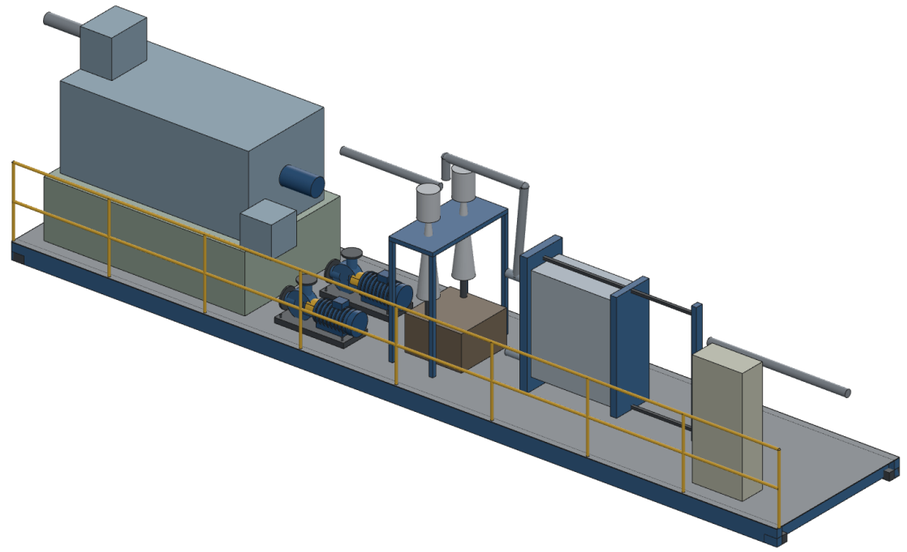
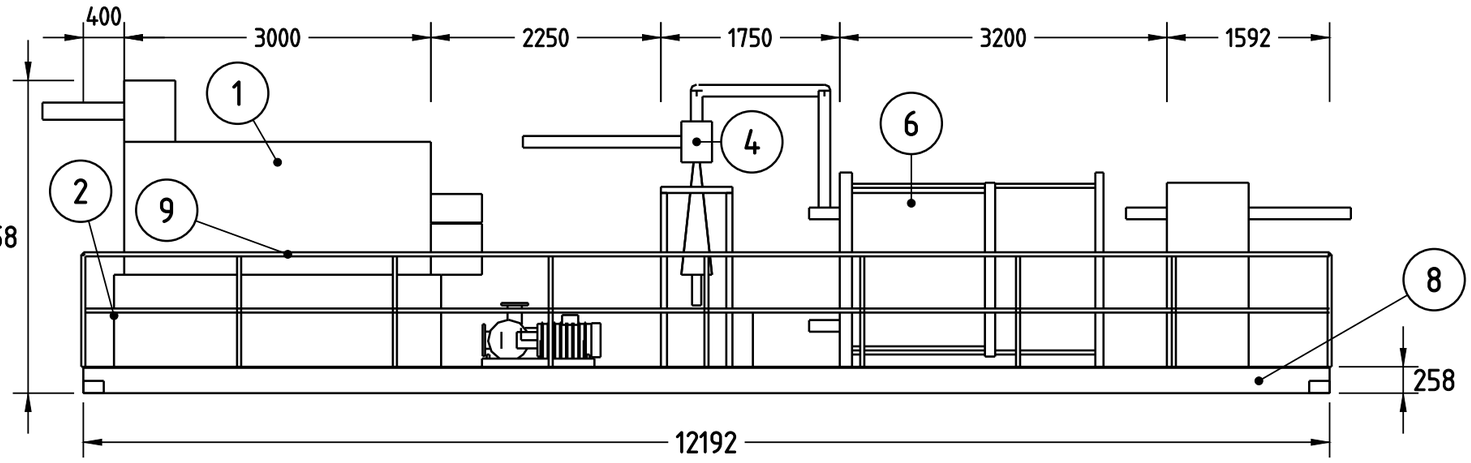


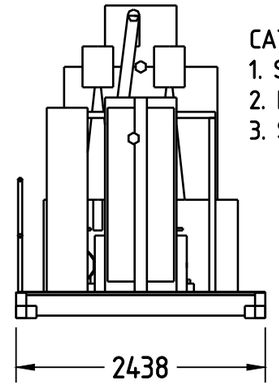

DENAH
SKALA 1:60



ISOMETRI (TANPA SKALA)




TAMPAK DEPAN
SKALA 1:60




TAMPAK UJUNG
SKALA 1:60

CATATAN :
1. Seluruh alat dirakit & diuji di bengkel.
2. Pengiriman: 1 truk trailer 40 ft, ± 12 t.
3. Sambungan: POME masuk DN150 (kiri), POME keluar DN100 ke TK-101 (kanan).

**DAFTAR BAGIAN**

| No | Tag | Uraian | Bahan | Jml | kg |
|---|---|---|---|---|---|
| 1 | SC-101 | Saringan drum Ø900x2600, 0,75 mm | SS304 | 1 | 1450 |
| 2 | – | Bak sump 3 m³ | SS304 t4 | 1 | 620 |
| 3 | P-101A/B | Pompa desander H 20 m, VSD | CD4MCu, 11 kW | 2 | 2x310 |
| 4 | HC-101 | Hidrosiklon Ø300 | PU-lined CS | 2 | 2x140 |
| 5 | – | Bak pasir 0,4 m³ | S275 galv. | 1 | 180 |
| 6 | E-101 | PHE 827 kWth | SS316/EPDM | 1 | 1850 |
| 7 | – | Panel kontrol lokal | IP65 | 1 | 220 |
| 8 | – | Skid UNP 250 12192x2438 | S275, cat | 1 | 3900 |
| 9 | – | Pegangan tangan Ø42,4 | S275 galv. | 1 | 240 |
| 10 | – | Pipa, katup, kabel | SS304 / PVC | 1 lot | 1100 |

**SAMBUNGAN SKID**

| Tag | Ukuran | Layanan | Dari → ke |
|---|---|---|---|
| N-A | DN150 | POME panas masuk (85 °C) | PKS → SC-101 |
| N-B | DN100 | POME tersaring ke TK-101 | E-101 → TK-101 |
| N-C | DN80 | Air pendingin masuk / keluar | CT-601 ↔ E-101 |
| N-D | DN50 | Underflow pasir | HC-101 → bak |
| N-E | – | Daya 400 V, 3 fasa, 45 kVA | MCC → panel |

| | | | | |
|---|---|---|---|---|
| University: UNIVERSITAS | Checked by : – | Design Lab. | Document type: Assembly Drawing | Rev: 0 |
| | Author : NAMA TIM | PM-1 Skid Praolah POME (SC-101, HC-101, E-101) | Unit: mm / Scale: 1 : 60 / Creation date: 15/10/2026 | Size: A3 |
| | Eng. Approved by : – | | BG-M-001 | Sheet number: 4 / 9 |