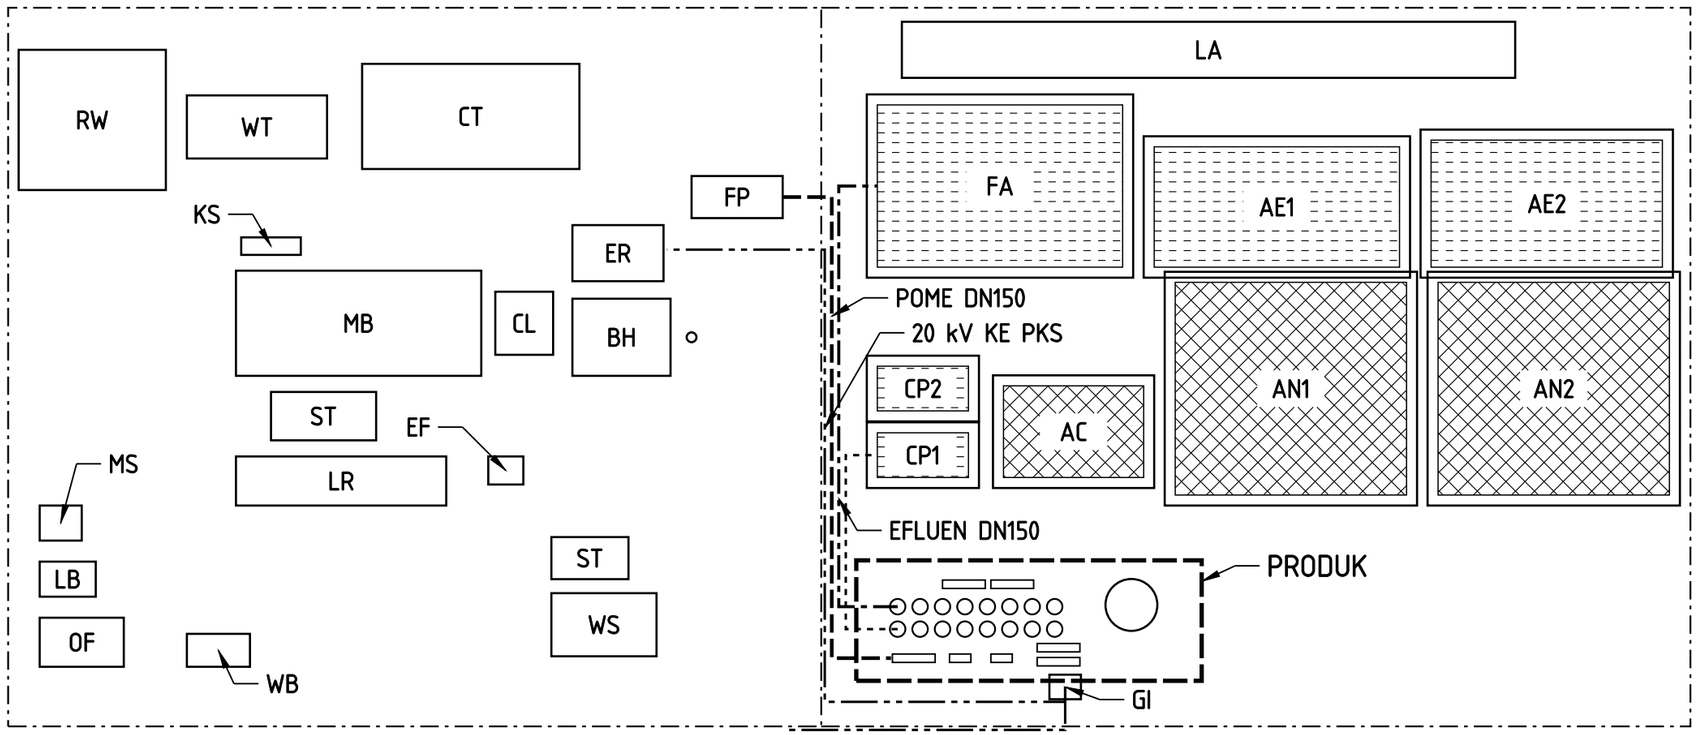

INTERKONEKSI		
Rute (model 3D)	m	USD
POME DN150 fat pit -> PM-1	162	22740
Efluen DN150 -> kolam polishing	148	10346
Bypass darurat -> kolam pendingin	73	5140
20 kV gardu -> jaringan PLN	92	4151
20 kV ke rumah mesin PKS + trafo	247	27874
Total (masuk CAPEX)		70251

LAHAN	
Luas lahan	m²
Kolam POME sebelum	22361
Kolam tetap (polishing)	11281
Kolam dibebaskan	11081
Plot produk	3387

PEMERIKSAAN JARAK AMAN			
Jarak aman	m	min	OK
Flare -> tepi GH	16.1	15	Ya
Flare -> kontainer CHP	30.5	15	Ya
GH -> rumah boiler PKS	142.9	30	Ya
GH -> tangki CPO	208.7	30	Ya
Flare -> batas pagar lokasi	17.2	10	Ya
Reaktor -> kolam pendingin (tanah)	20.6	20	Ya
Cerobong boiler -> GH	138.2	30	Ya

CATATAN :
1. Arsir silang = kolam dibebaskan; arsir putus = air.
2. Efluen produk tetap ke kolam polishing sebelum aplikasi lahan.
3. Garis rantai = kabel 20 kV (PKS & PLN).

JALAN UMUM

250 m

DENAH LOKASI (DARI MODEL 3D)

SKALA 1:1750

LEGENDA	
Kode	Uraian
WB	Jembatan timbang 2 x 60 t
OF	Kantor
LB	Laboratorium
WS	Bengkel
ST	Gudang
MS	Musala
LR	Loading ramp TBS 20 pintu
ST	Rebusan 3 x 30 m
MB	Pabrik utama
CL	Stasiun klarifikasi (CST, tangki minyak)
KS	Silo kernel
BH	Rumah boiler 2 x 30 t uap/jam
ER	Rumah mesin
RW	K. air baku
WT	Pengolahan air + menara air

Kode	Uraian
CT	Tangki CPO 2 x 2.000 t
EF	Hopper TKS
FP	Fat pit (sumber POME)
CP1	K. pendingin 1 (585 m³, 1 d)
CP2	K. pendingin 2 (585 m³, 1 d)
AC	K. pengasaman (2,925 m³, 5 d) (bebas)
AN1	K. anaerobik 1 (17,550 m³, 30 d) (bebas)
AN2	K. anaerobik 2 (17,550 m³, 30 d) (bebas)
FA	K. fakultatif (8,775 m³, 15 d)
AE1	K. aerobik 1 (4,388 m³, 7.5 d)
AE2	K. aerobik 2 (4,388 m³, 7.5 d)
LA	Flatbed aplikasi lahan (efluen ke kebun)
GI	Gardu step-up 0,4/20 kV 1,25 MVA
PRODUK	Set biogas portabel, plot 3387 m²

University: UNIVERSITAS	Checked by : -	Design Lab.	Document type: Site Plan	Rev: 0
	Author : NAMA TIM	Denah Lokasi PKS 45 t TBS/jam + Set Generator Biogas	Unit: mm / Scale: 1 : 1750 / Creation date: 15/10/2026	Size: A3
	Eng. Approved by : -		BG-GA-002	Sheet number: 9 / 9