

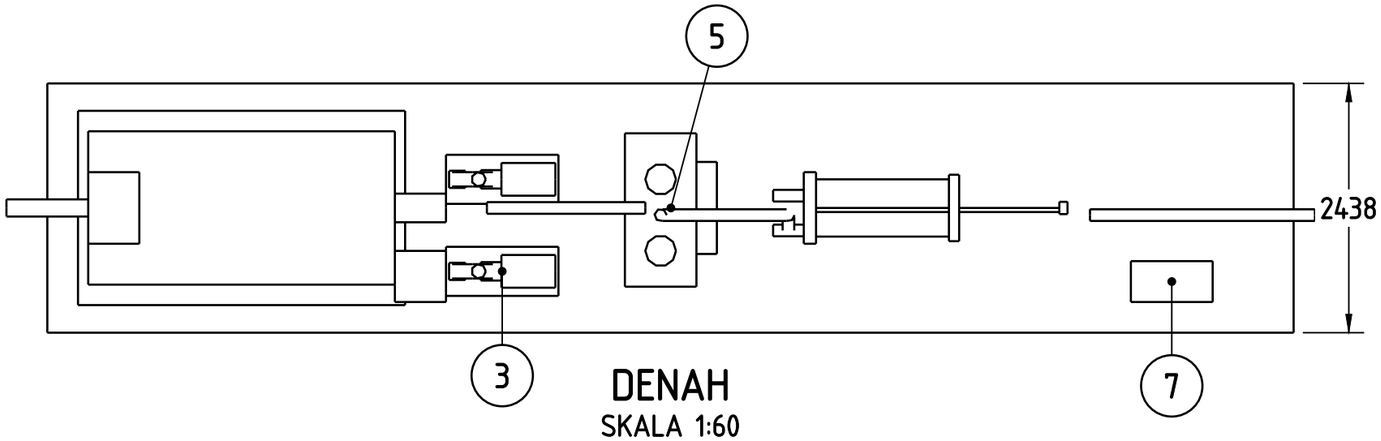



DENAH
SKALA 1:60

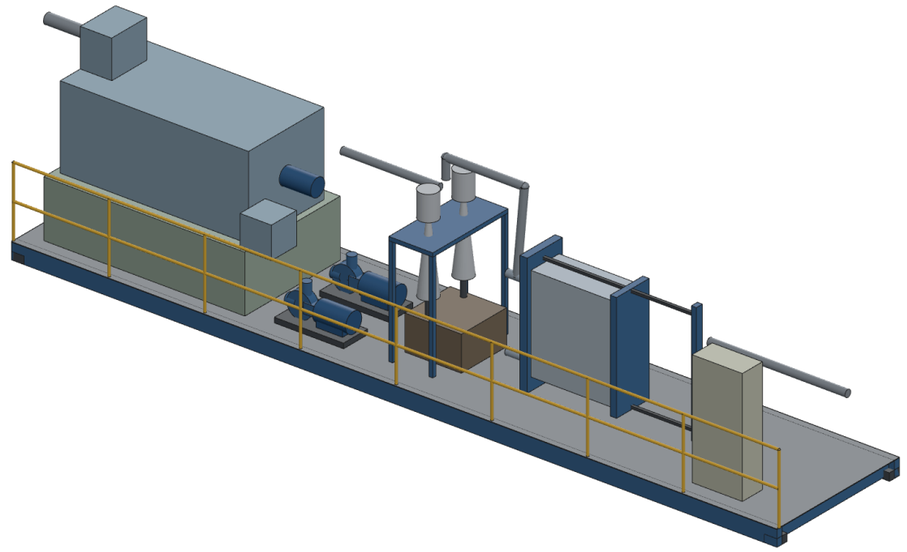

ISOMETRI (TANPA SKALA)

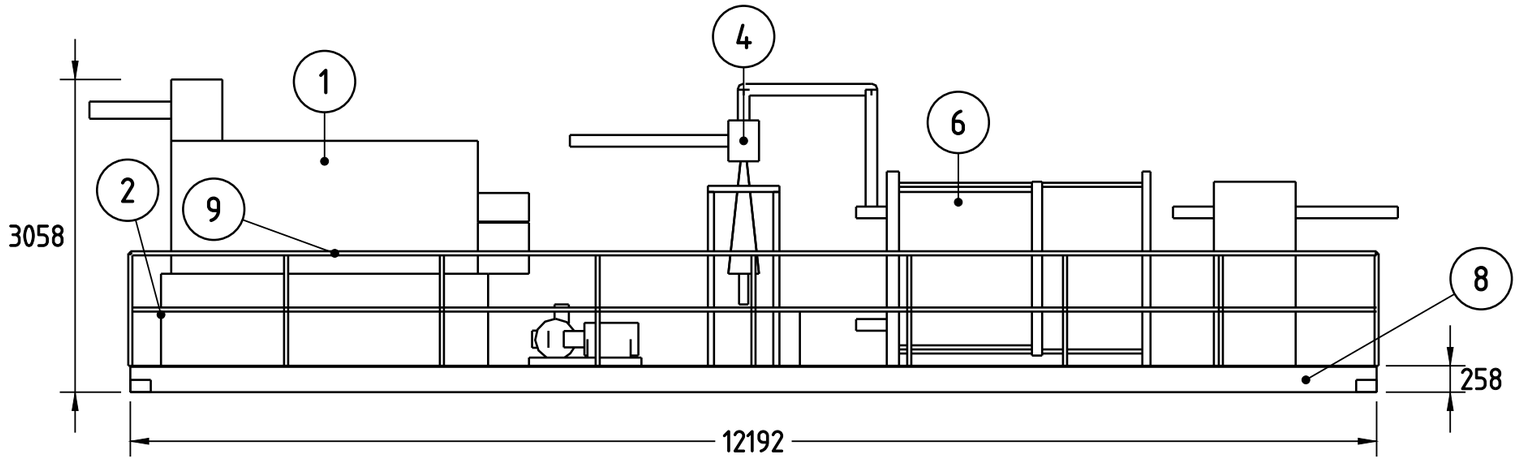

TAMPAK DEPAN
SKALA 1:60

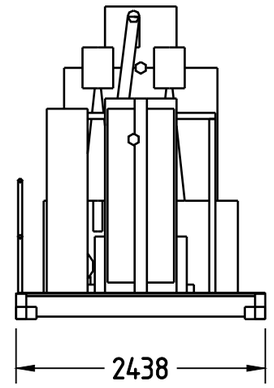

TAMPAK UJUNG
SKALA 1:60

CATATAN :
1. Seluruh alat dirakit & diuji di bengkel.
2. Pengiriman: 1 truk trailer 40 ft, ± 12 t.
3. Sambungan: POME masuk DN150 (kiri), POME keluar DN100 ke TK-101 (kanan).

DAFTAR BAGIAN			
No	Tag	Uraian	Jml
1	SC-101	Saringan drum putar Ø900 x 2600, celah 0,75 mm, 24.4 m³/jam	1
2	–	Bak sump 3 m³ di bawah saringan	1
3	P-101A/B	Pompa umpan desander, H 20 m, VSD	2
4	HC-101	Hidrosiklon desander 2 x Ø300	2
5	–	Bak pasir (grit bin) 0,4 m³	1
6	E-101	Pendingin POME pelat 812 kWth, SS316	1
7	–	Panel kontrol lokal	1
8	–	Skid baja UNP 250, 12192 x 2438	1
9	–	Pegangan tangan Ø42,4	1

University: UNIVERSITAS	Checked by : –	Design Lab.	Document type: Assembly Drawing			Rev: 0
	Author : NAMA TIM	PM-1 Skid Praolah POME (SC-101, HC-101, E-101)	Unit: mm	Scale: 1 : 60	Creation date: 15/10/2026	Size: A3
	Eng. Approved by : –		BG-M-001			Sheet number: 4 / 8