

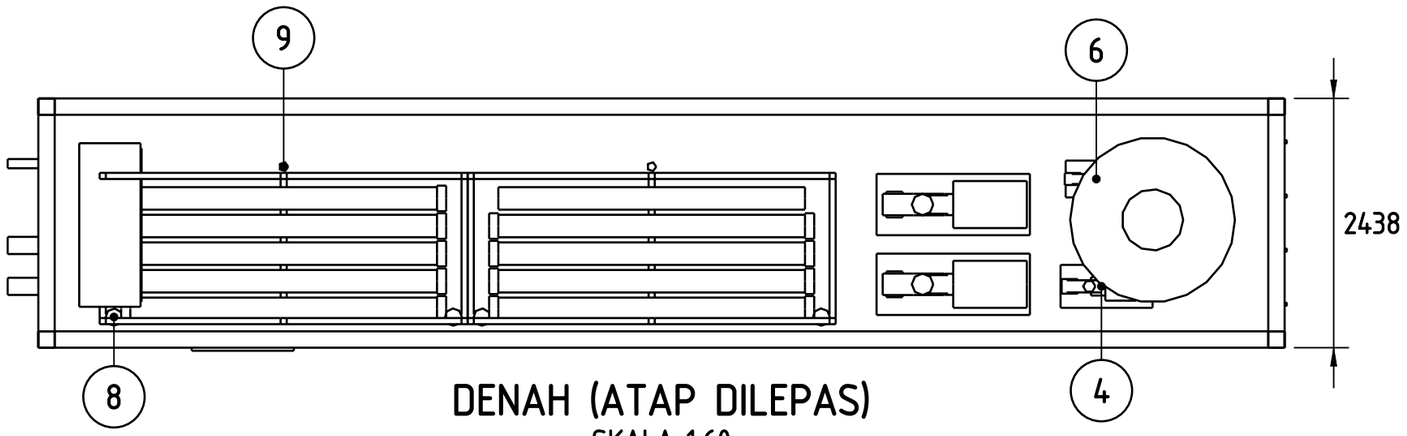



DENAH (ATAP DILEPAS)
SKALA 1:60

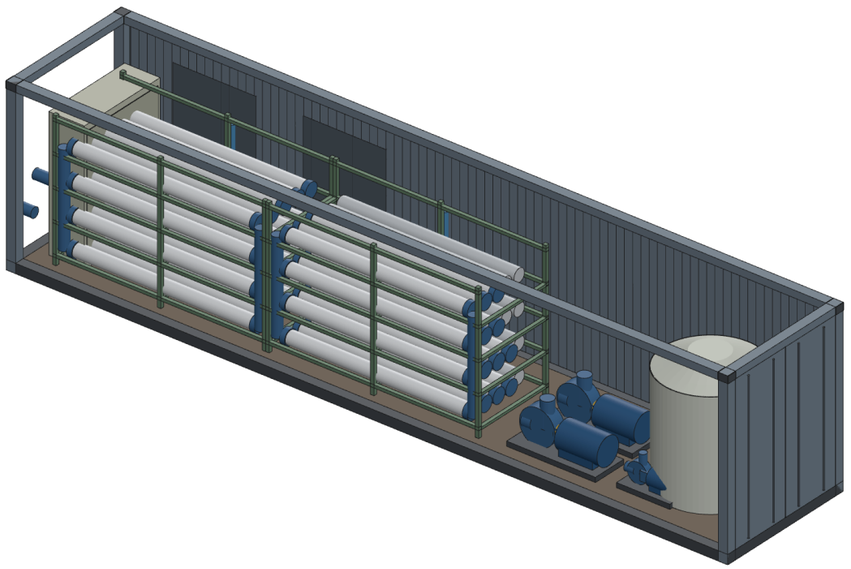

ISOMETRI POTONG (TANPA SKALA)

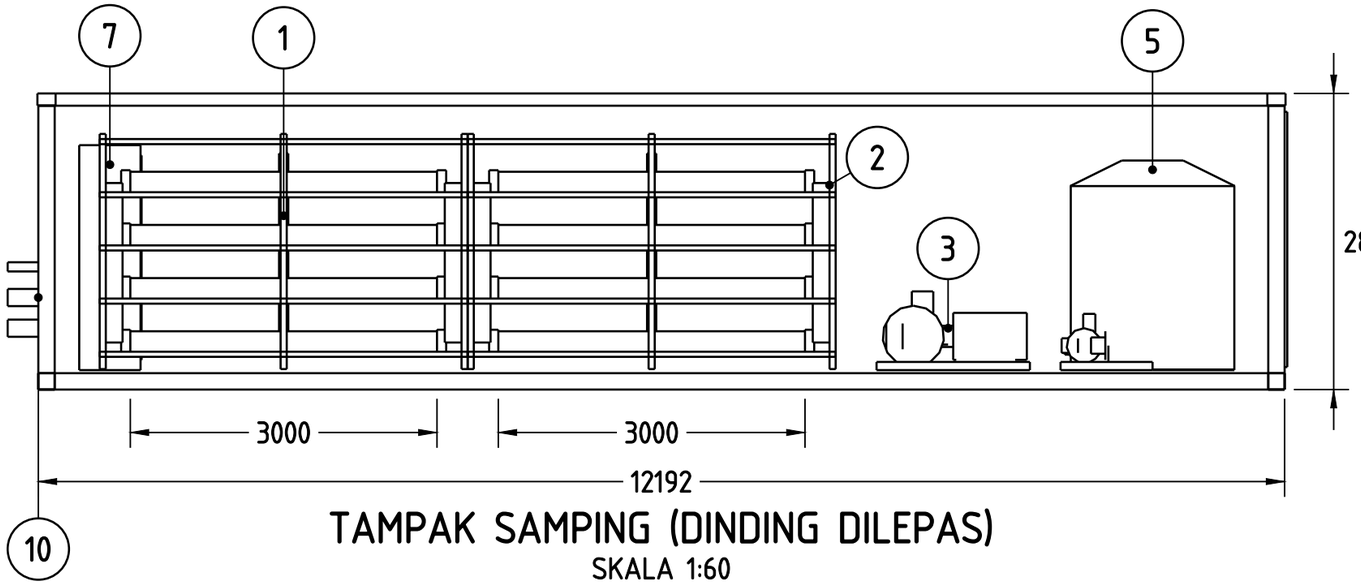

TAMPAK SAMPING (DINDING DILEPAS)
SKALA 1:60

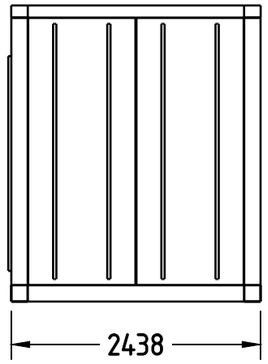

TAMPAK UJUNG
SKALA 1:60

CATATAN :
1. Modul 2 bank x 5 kolom x 4 tingkat (40 posisi), jarak antar tingkat 520 mm.
2. Fluks rancangan 15 LMH, luas total 996 m².
3. Massa angkut ± 16 t; kontainer ISO 40 ft HC.
4. Lorong servis 850 mm di sisi pompa.
5. Dinding kiri & atap dilepas pada tampak / denah untuk kejelasan.

DAFTAR BAGIAN			
No	Tag	Uraian	Jml
1	MB-301	Modul UF tubular Ø220 x 3000, 30 m²	34 (+6 cad.)
2	–	Rak modul baja galvanis 2 bank	2
3	P-301A/B	Pompa cross-flow 149 m³/jam, 30 kW	2
4	P-302	Pompa permeat, VSD	1
5	TK-302	Tangki CIP Ø1600 x 1800, 4 m³	1
6	P-304	Pompa CIP	1
7	–	Panel MCC + PLC membran	1
8	–	Header umpan / retentat DN150	4
9	–	Header permeat DN80	2
10	–	Nosel dinding ke reaktor (DN150/80)	3
11	–	Kontainer ISO 40 ft HC, kisi ventilasi + pintu samping	1

University: UNIVERSITAS	Checked by : –	Design Lab.	Document type: Assembly Drawing			Rev: 0
	Author : NAMA TIM	PM-4 Kontainer Membran UF (MB-301, P-301, P-302, TK-302)	Unit: mm	Scale: 1 : 60	Creation date: 15/10/2026	Size: A3
	Eng. Approved by : –		BG-M-004			Sheet number: 3 / 8