

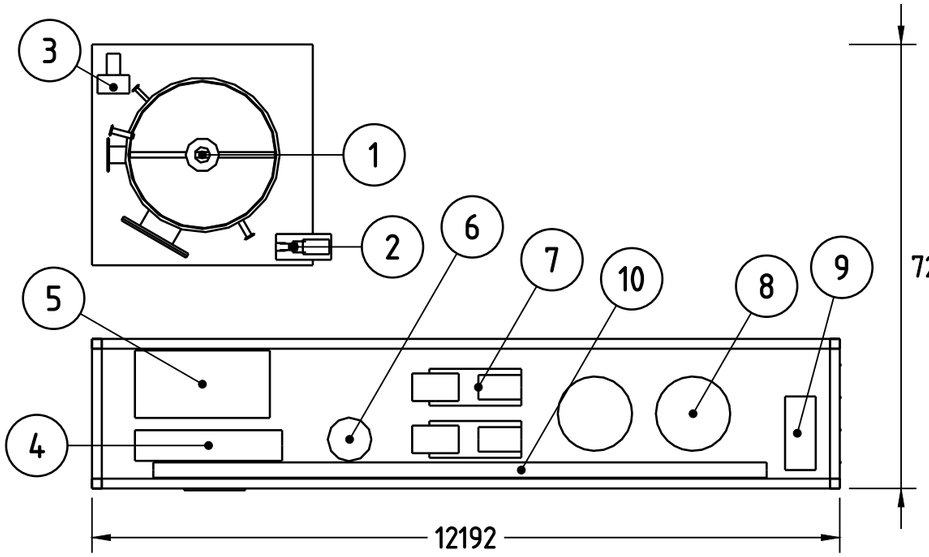



DENAH (ATAP DILEPAS)
SKALA 1:100

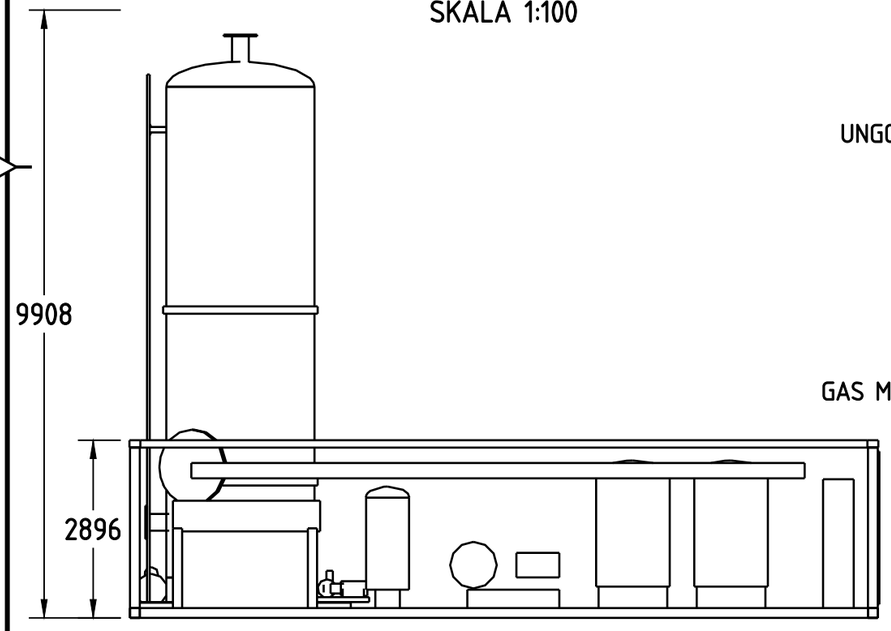

TAMPAK DEPAN (DINDING DILEPAS)
SKALA 1:100

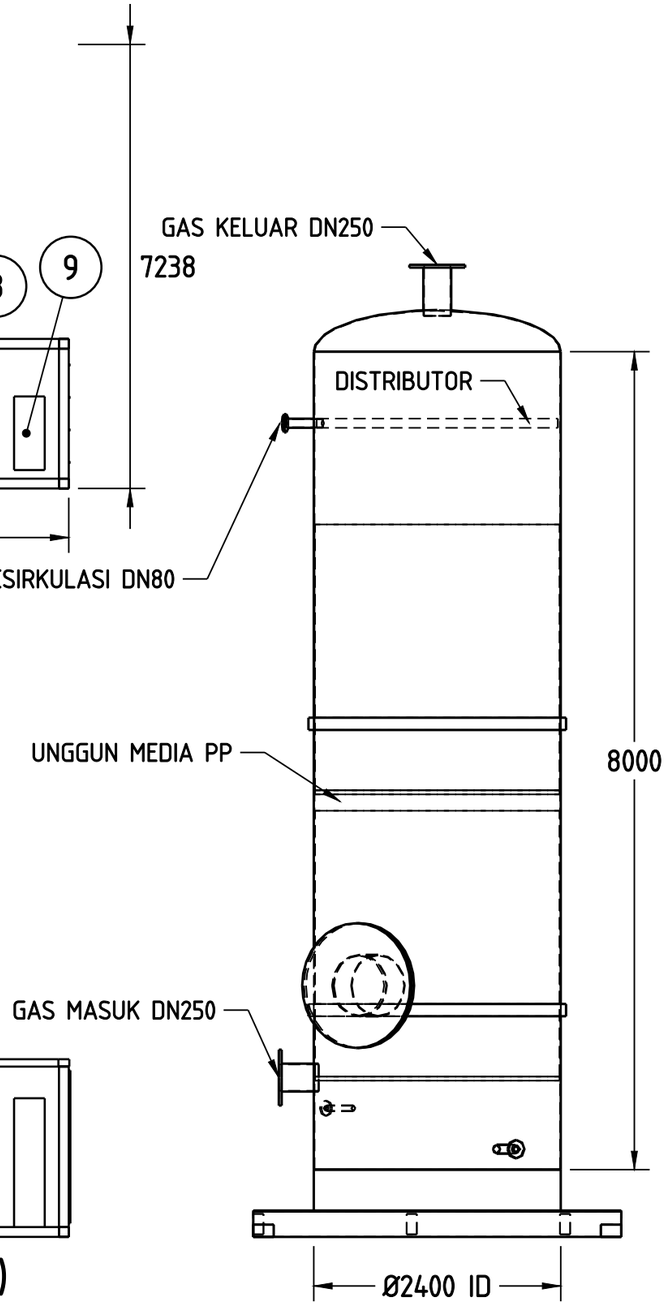

BTF-301 (ELEVASI)
SKALA 1:60

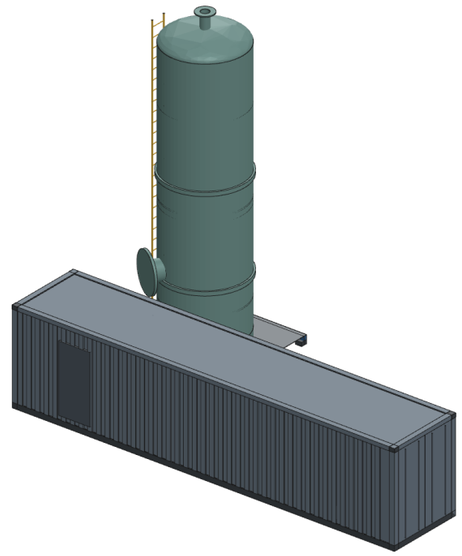

ISOMETRI (TANPA SKALA)

DAFTAR BAGIAN			
No	Tag	Uraian	Jml
1	BTF-301	Bio-trickling filter Ø2400 x 8000, media PP 16.4 m³	1
2	P-305	Pompa resirkulasi nutrien BTF	1
3	K-301	Blower udara BTF 5.6 Nm³/jam	1
4	HX-301	Pendingin gas shell-tube, 15.3 kWth	1
5	CH-301	Chiller paket berpendingin udara	1
6	V-301	KO pot Ø700 + demister	1
7	K-302A/B	Blower biogas 537 m³/jam, ΔP 20 kPa	2
8	AC-301A/B	Filter karbon aktif Ø1200, 2 bed	2
9	–	Panel kontrol + analis gas	1
10	–	Header gas DN250	1
11	–	Kontainer ISO 40 ft HC (ATEX zona 2)	1
12	–	Skid BTF 3600 x 3600 + tangga	1

CATATAN :
1. BTF dikirim sebagai bejana terpisah di trailer.
2. H_2S: 2887 ppm masuk → 34 ppm ke genset.
3. Kontainer: ventilasi paksa + detektor gas.

University: UNIVERSITAS	Checked by : –	Design Lab.	Document type: Assembly Drawing			Rev: 0
	Author : NAMA TIM	PM-6 Skid Pengolahan Biogas (BTF-301, K-302, AC-301)	Unit: mm	Scale: 1:100 / 1:60	Creation date: 15/10/2026	Size: A3
	Eng. Approved by : –		BG-M-006			Sheet number: 5 / 8